
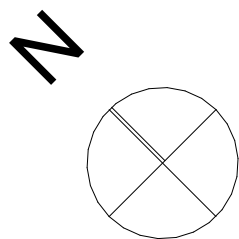


TOTALT I BYGGET; 16 STK LEILIGHETER,
(HVORAV 8 STK HAR UNIVERSELT
TILGJENGELIG BAD)

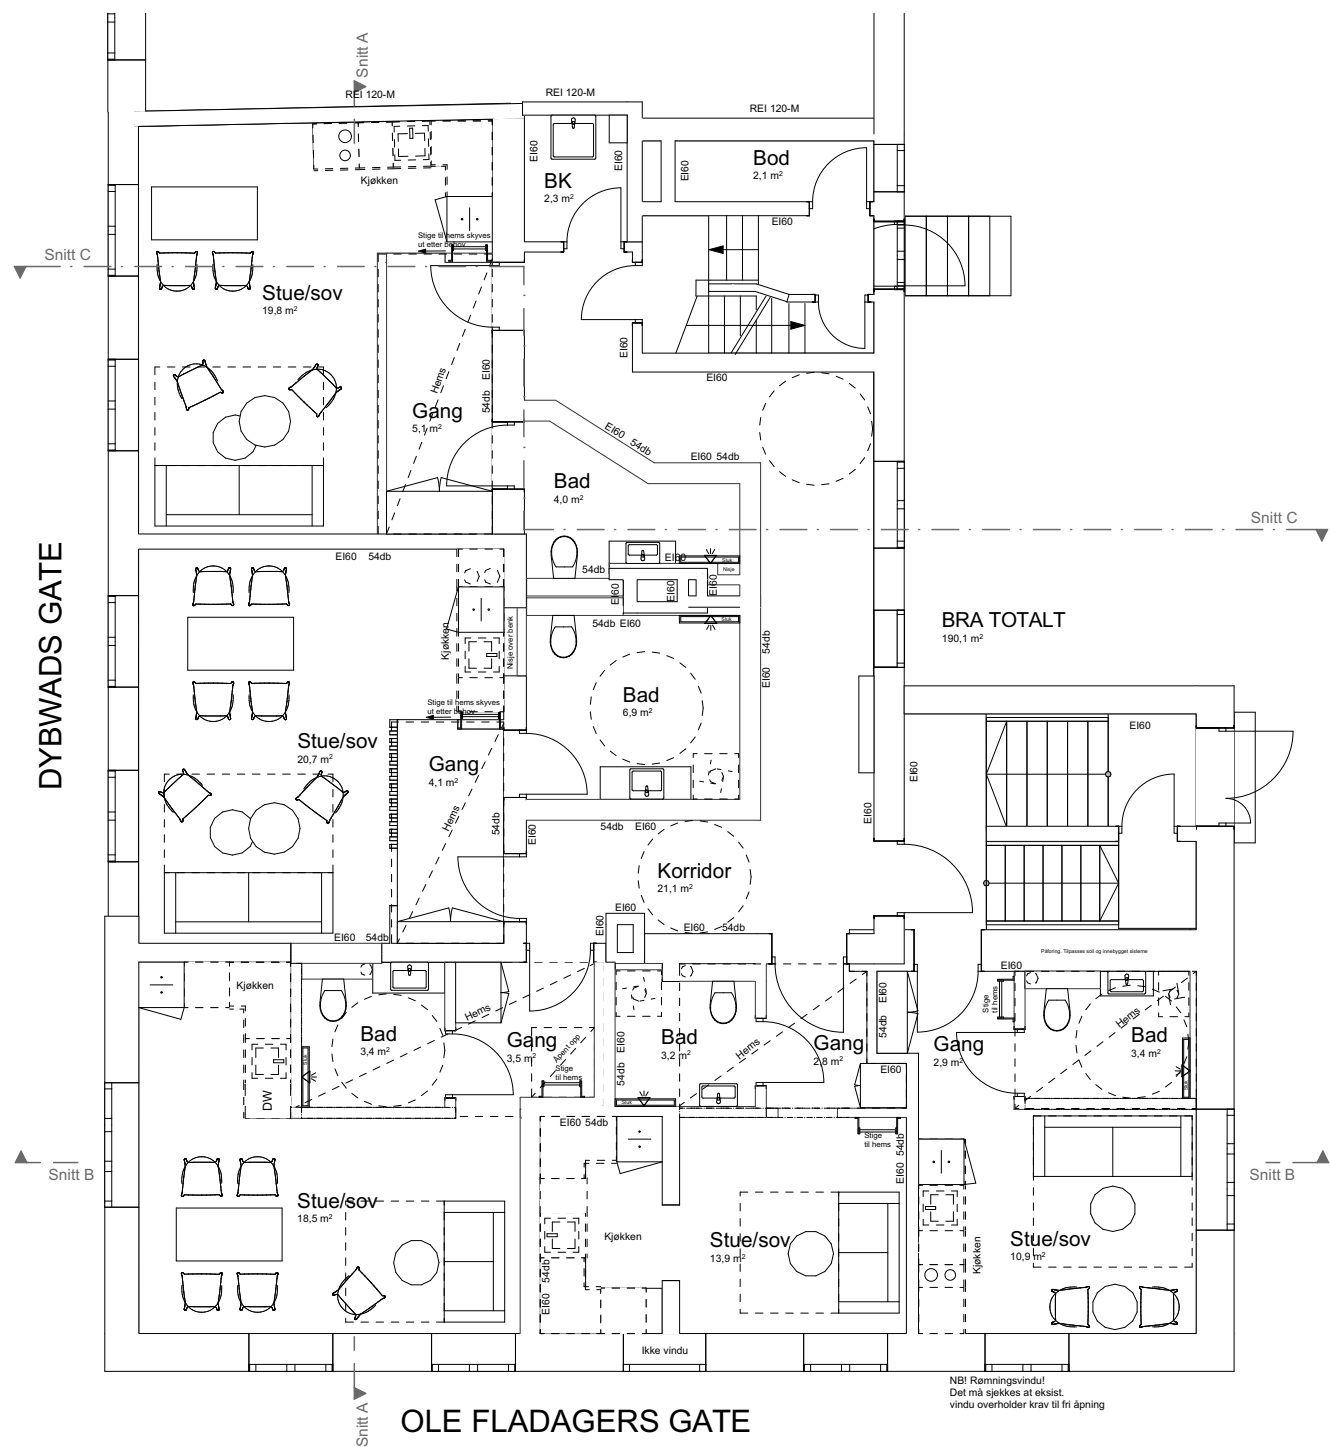

B	Mindre justeringer etter oppmåling	08.05.25	ABS	CN
A	Heis fjernet	20.06.22	ABS	CE
Rev	Beskrivelse	Dato	Sign	Kontr

MEDVIND ARKITEKTUR

Fase BYGGESØKNAD	Sign. ABS
Tiltakshaver Landlord Eiendom AS	Kontroll CE
	Dato 18.03.22
Prosjekt Dybwads gate 8 Oslo	Målestokk 1:100 Gnr./Bnr./Festenr.: 215/52
Type tegning: Plan 1. Etasje	Rev. B
Prosjektnr.: 1110	