


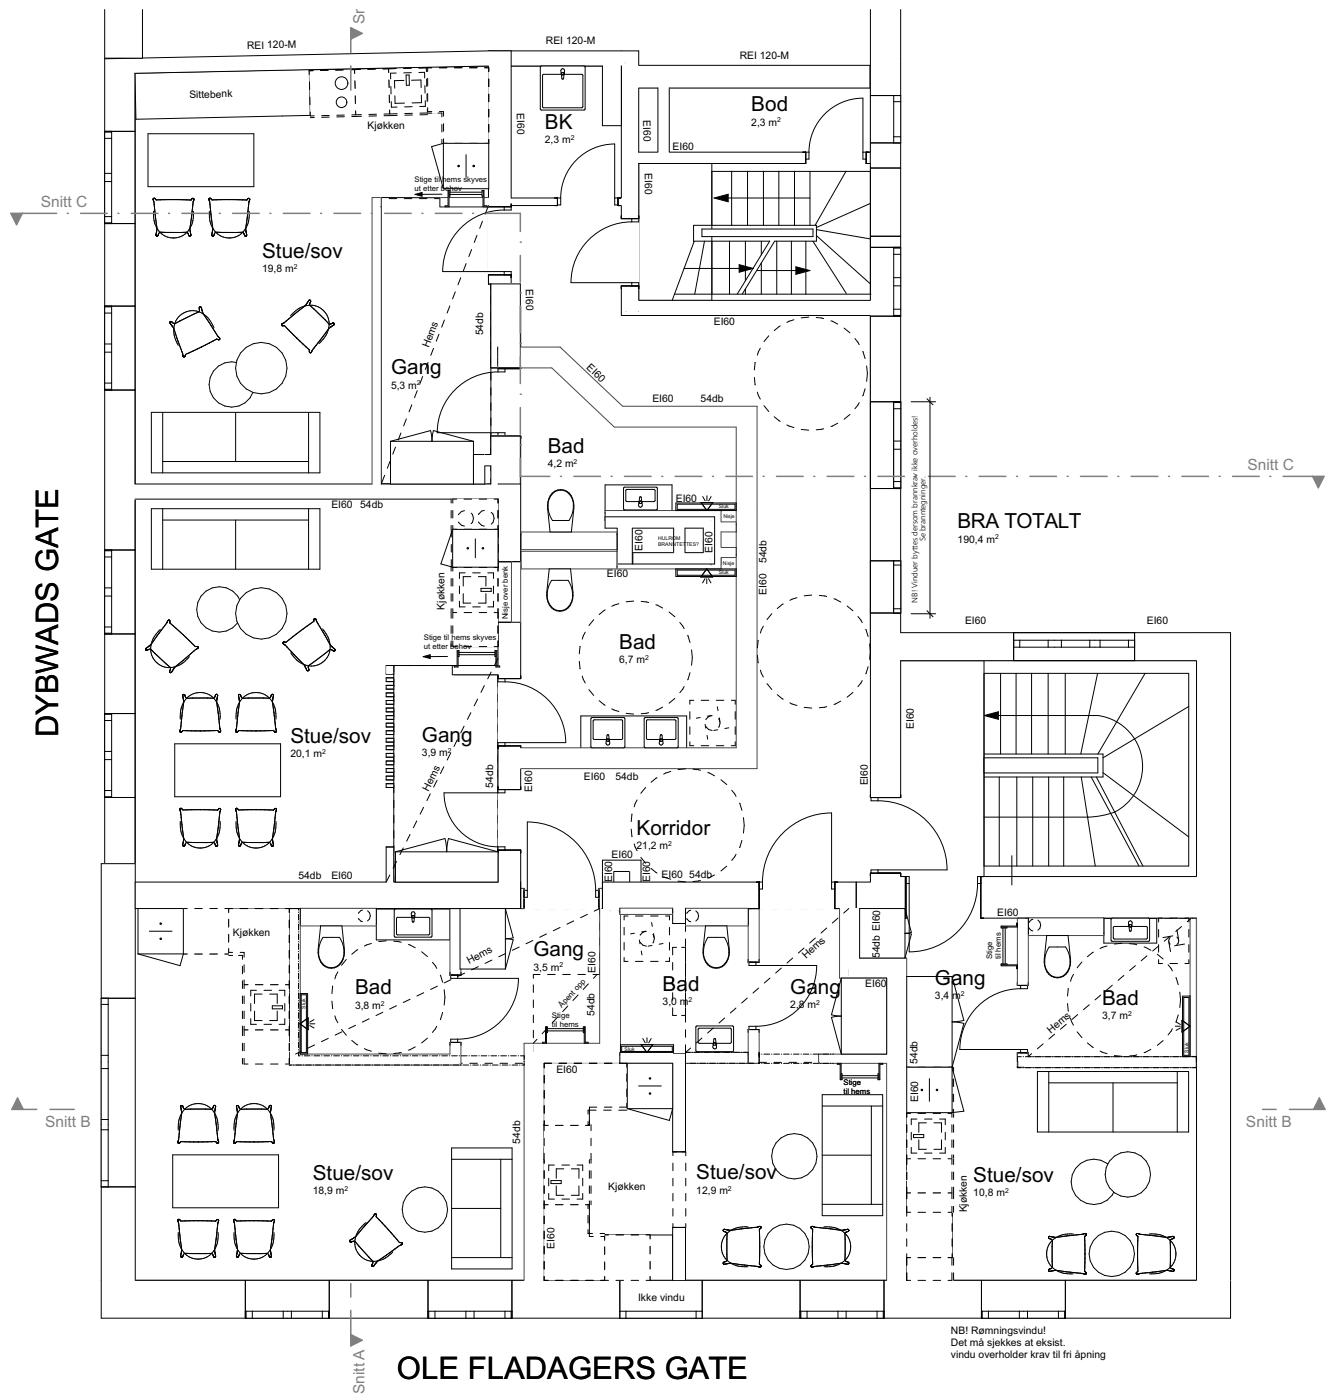

B	Mindre justeringer etter oppmåling	08.05.25	ABS	CN
A	Heis fjernet	20.06.22	ABS	CE
Rev	Beskrivelse	Dato	Sign	Kontr
MEDVIND ARKITEKTUR				
Fase BYGGESØKNAD		Sign. ABS		
Tiltakshaver Landlord Eiendom AS		Kontroll CE		
		Dato 18.03.22		
Prosjekt Dybwads gate 8 Oslo		Målestokk 1:100 Gnr./Bnr./Festenr.: 215/52		
Type tegning: 2.Etasje		Rev: B		
Prosjektnr.: 1110				